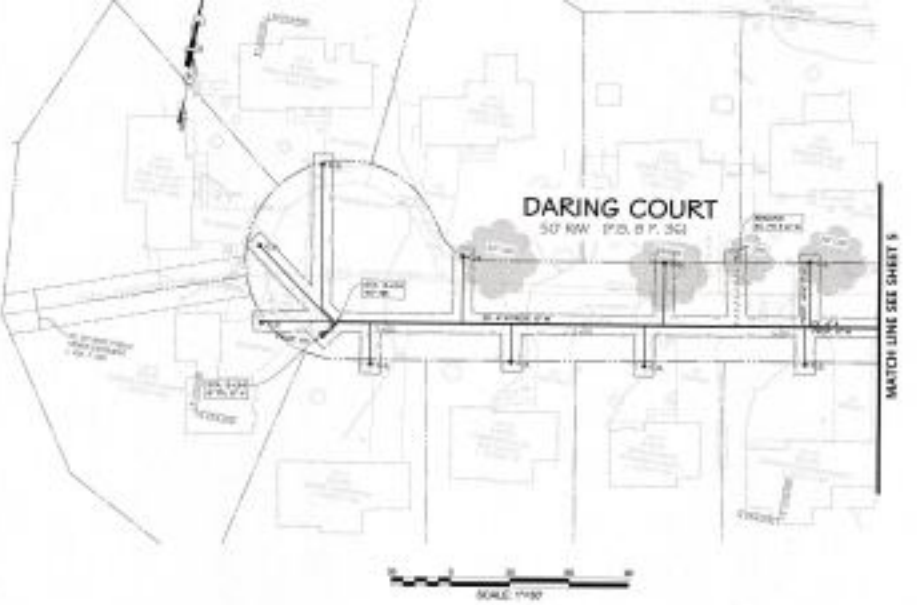

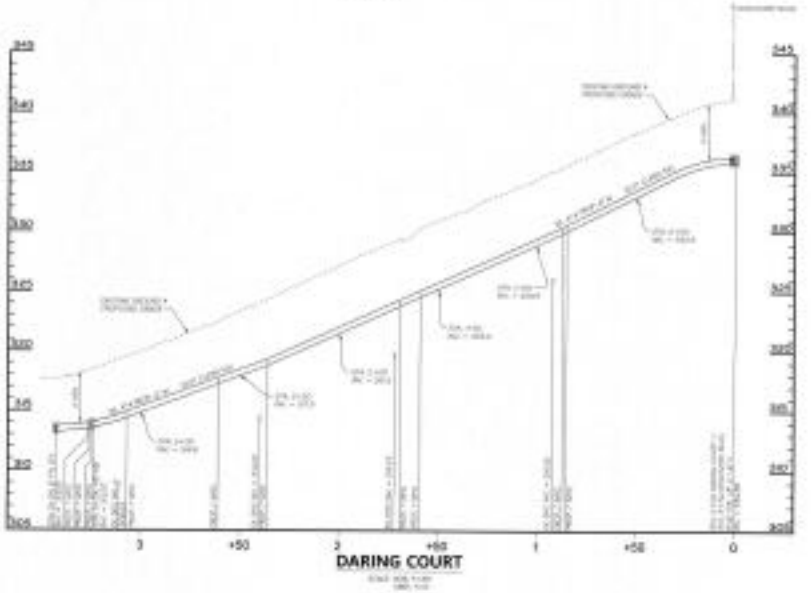

DMW

DARING COURT
PLAN & PROFILE

DISCOVERY PHASE - I
WATER MAIN
REPLACEMENT PROGRAM

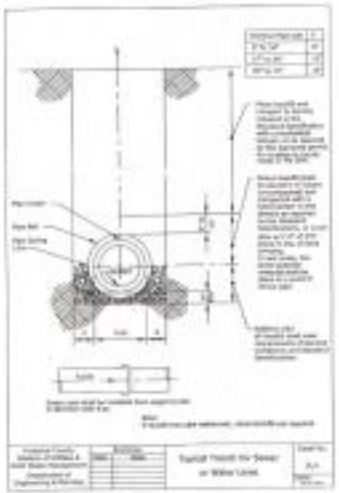

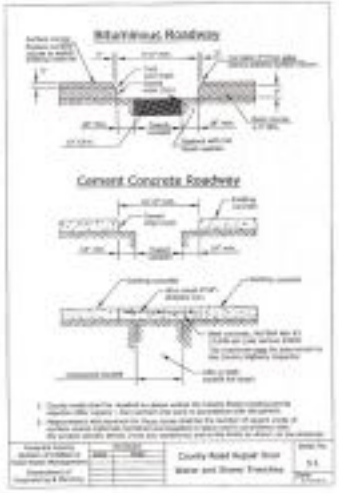

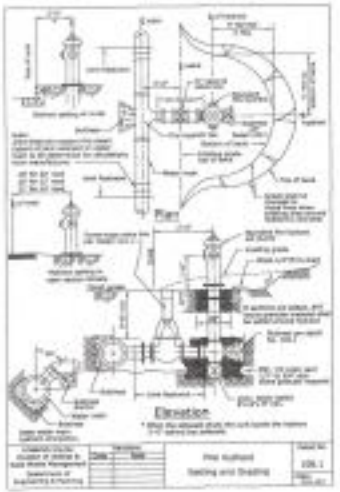

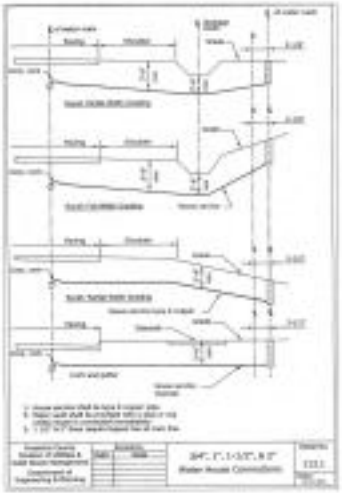

TRAFFIC CONTROL GENERAL NOTES:

TRAFFIC CONTROL SEQUENCE OF CONSTRUCTION

CONSTRUCTION PHASING

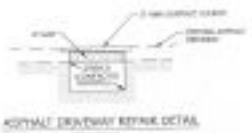

ASPHALT DRIVEWAY REPAIR DETAIL

TEMPORARY BYPASS PIPING NOTES

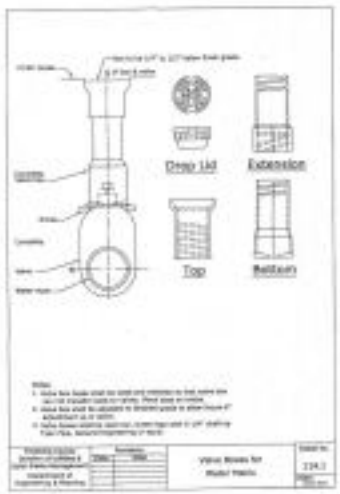

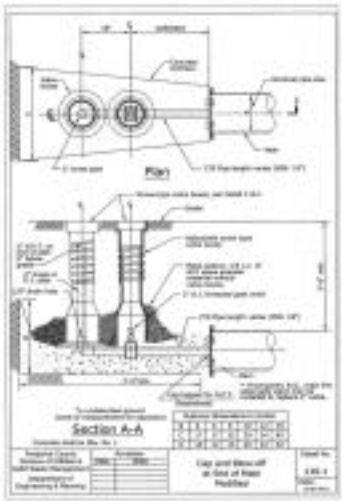

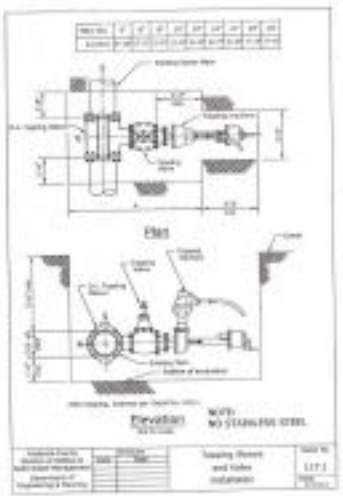

FOR UTILITY WORK THAT MAY BE PERFORMED BY UTILITY COMPANIES

FREDERICK COUNTY PUBLIC WORKS DIVISION

CALL MISS UTILITY AT 1-800-257-7777 FOR LOCATION OF UTILITIES AT LEAST 5 DAYS PRIOR TO BEGINNING CONSTRUCTION

DMW

WATER NOTES & DETAILS

DISCOVERY PHASE - I
WATER MAIN
REPLACEMENT PROGRAM

OWNER / DEVELOPER

DATE	BY	REVISIONS
09/09/2024	DMW	COUNTY & PUBLIC COMMENTS
12/02/2024	DMW	PWA ISSUED COMMENTS

INITIAL SUBM.	07/29/2024
SCALE:	AS SHOWN
DRAWN:	DMW
DESIGNED:	DMW
CHECKED BY:	DMW
PROJECT NO.:	2023-002
DRAWING:	2 of 16

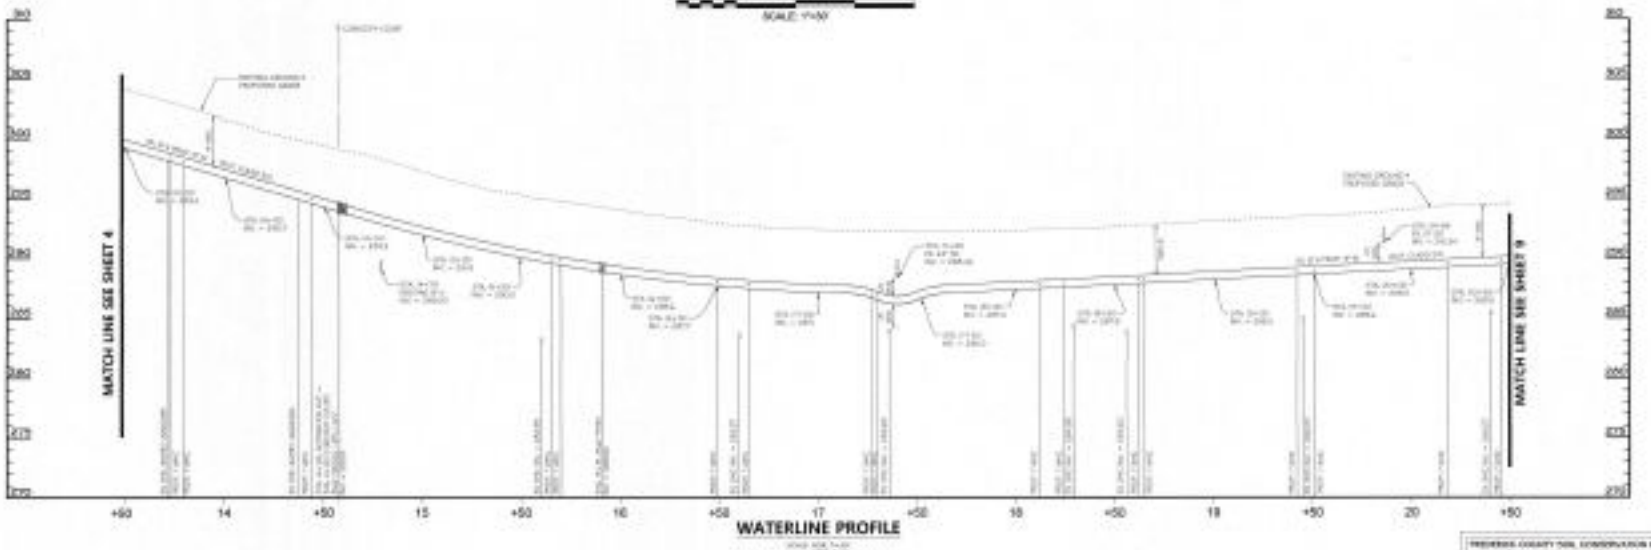

INSPIRATION AVENUE
PLAN & PROFILE

DISCOVERY PHASE - I
WATER MAIN
REPLACEMENT PROGRAM

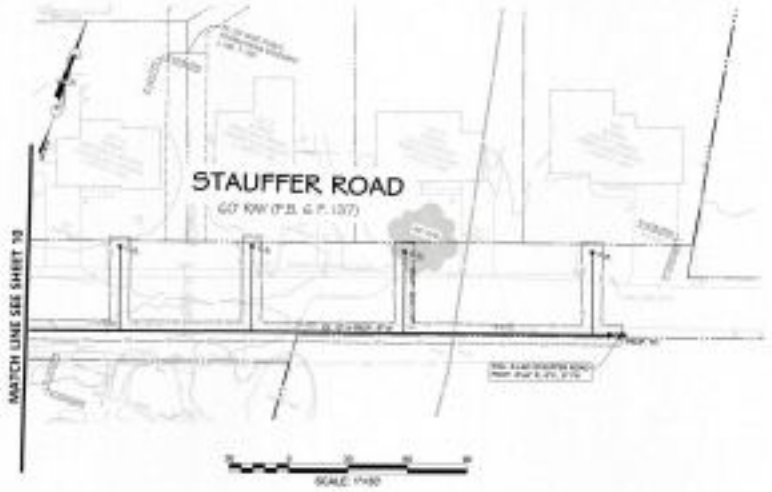

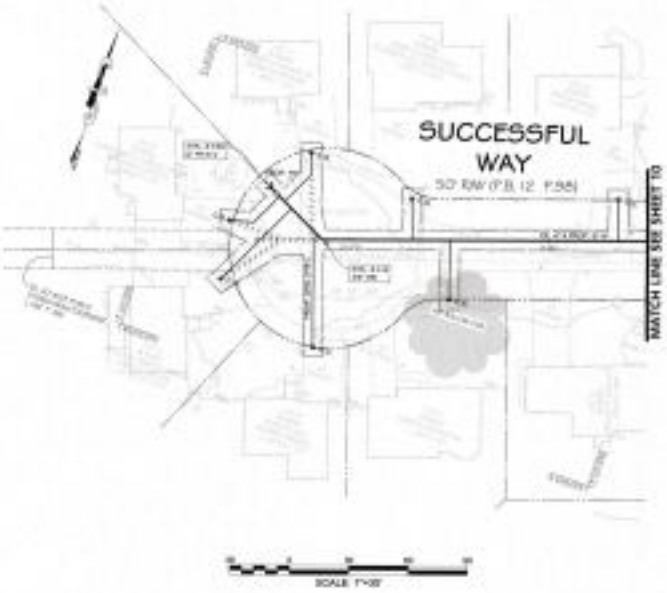

STAUFFER RO
SUCESSFUL W
PLAN & PROF
DISCOVERY PH
WATER MAIN
REPLACEMENT PRO

CALL MISS UTILITY AT 1-800-257-7777
FOR UTILITY LOCATIONS AT LEAST 3 DAYS
PRIOR TO BEGINNING CONSTRUCTION.

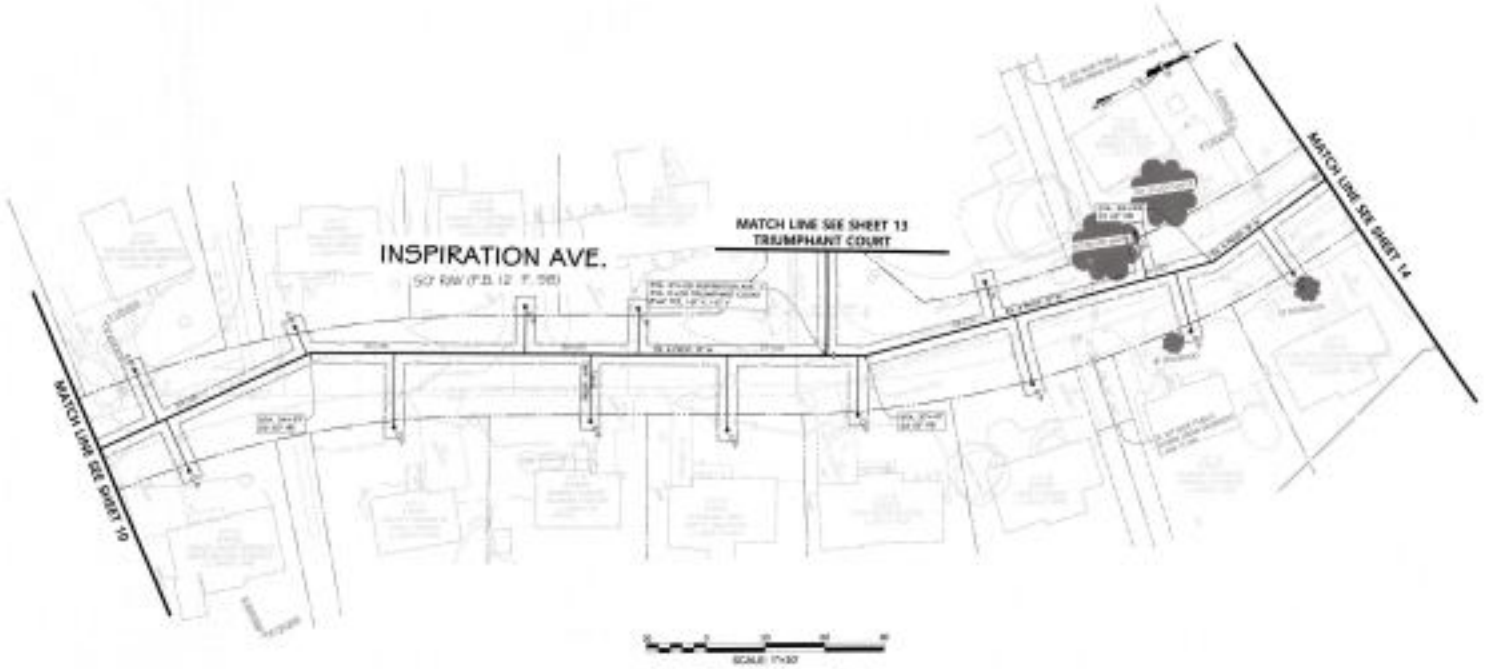

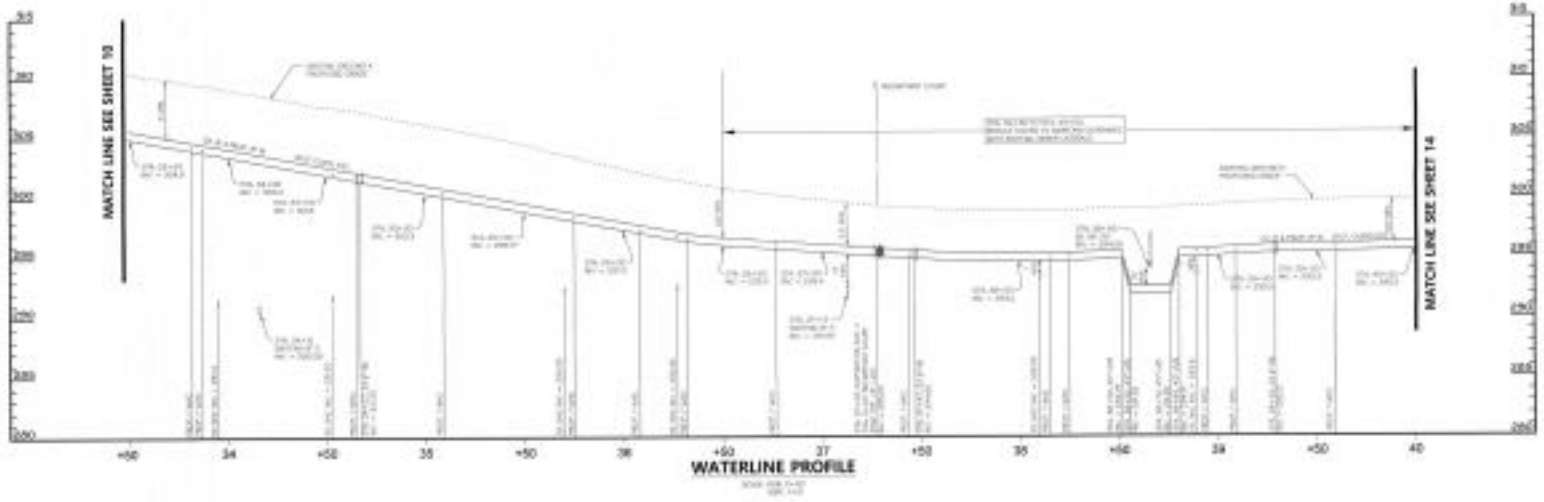

WATERLINE PROFILE

INSPIRATION AVENUE
PLAN & PROFILE

DISCOVERY PHASE - I
WATER MAIN
REPLACEMENT PROGRAM

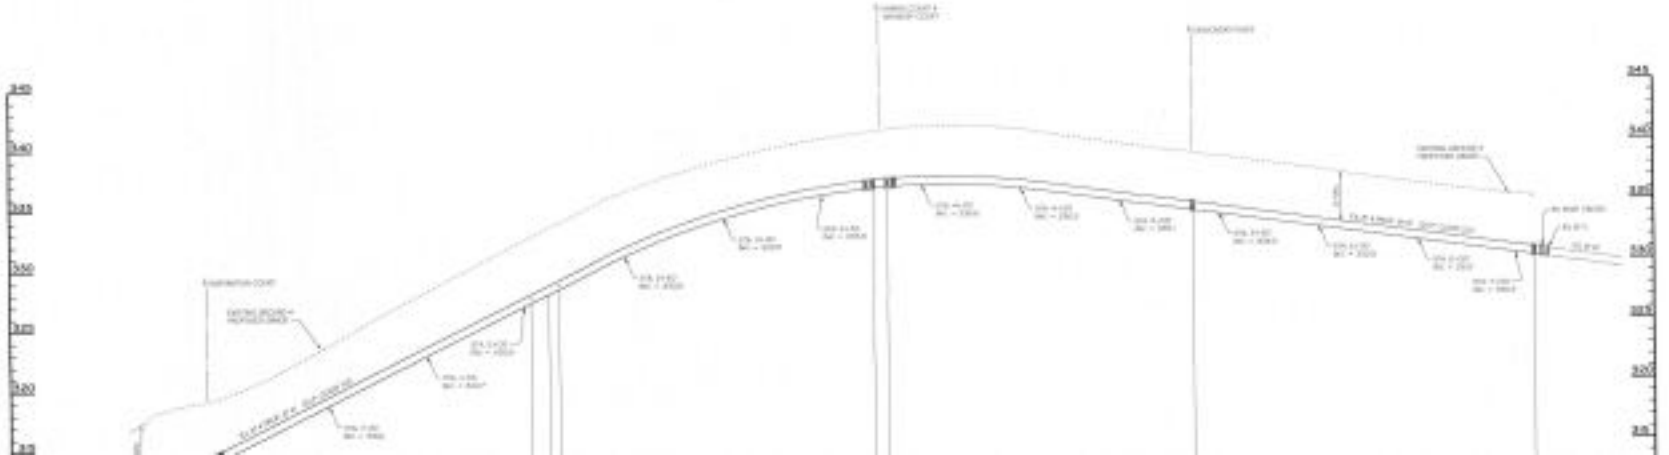

DISCOVERY BLVD.
PLAN & PROFILE

DISCOVERY PHASE - I
WATER MAIN
REPLACEMENT PROGRAM

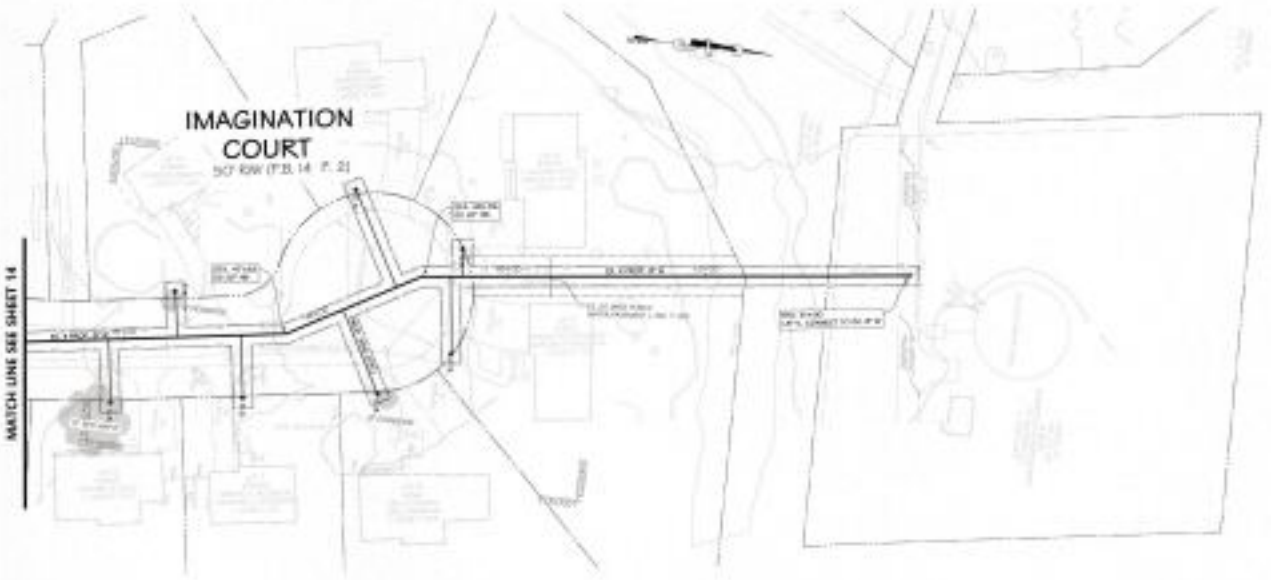

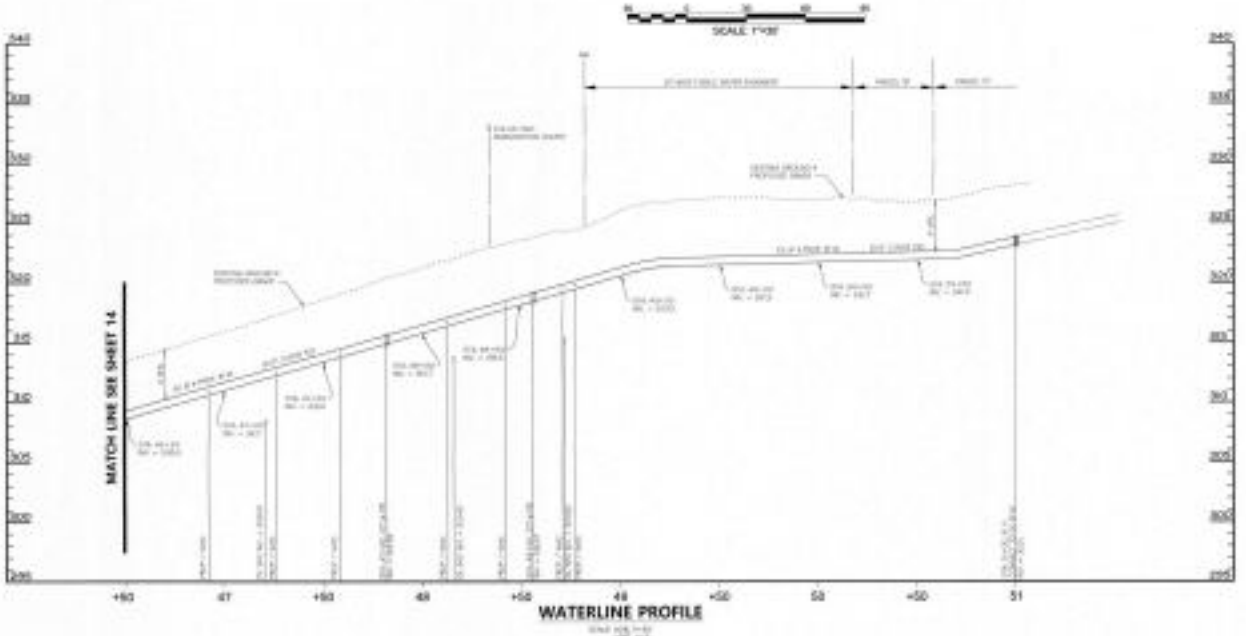

WATERLINE PROFILE

FREDERICK COUNTY SOIL CONSERVATION DISTRICT

CALL MISS UTILITY AT 1-800-257-7777 FOR UTILITY LOCATIONS AT LEAST 5 DAYS PRIOR TO BEGINNING CONSTRUCTION.

DMW

IMAGINATION COURT
PLAN & PROFILE

DISCOVERY PHASE - I
WATER MAIN
REPLACEMENT PROGRAM

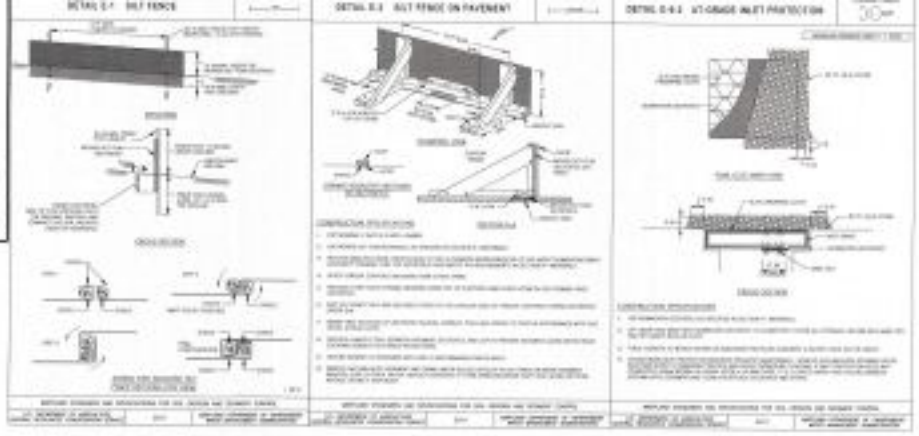

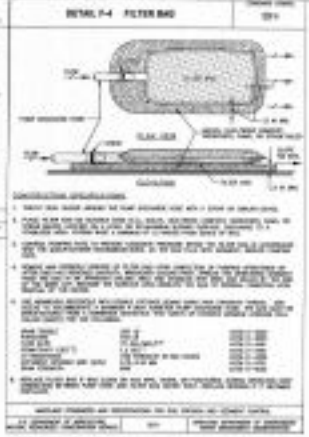

SCALE: 1"=30'

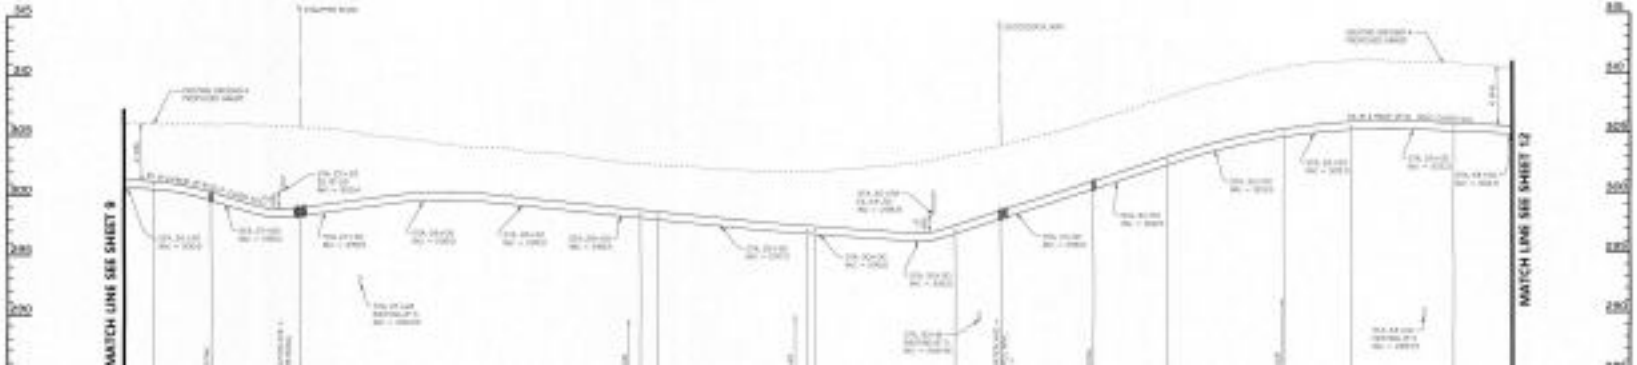

PASADENA COUNTY SOIL CONSERVATION DISTRICT

DATE: 7/17/2017

DMW

INSPIRATION AVENUE
PLAN & PROFILE

DISCOVERY PHASE - I
WATER MAIN
REPLACEMENT PROGRAM

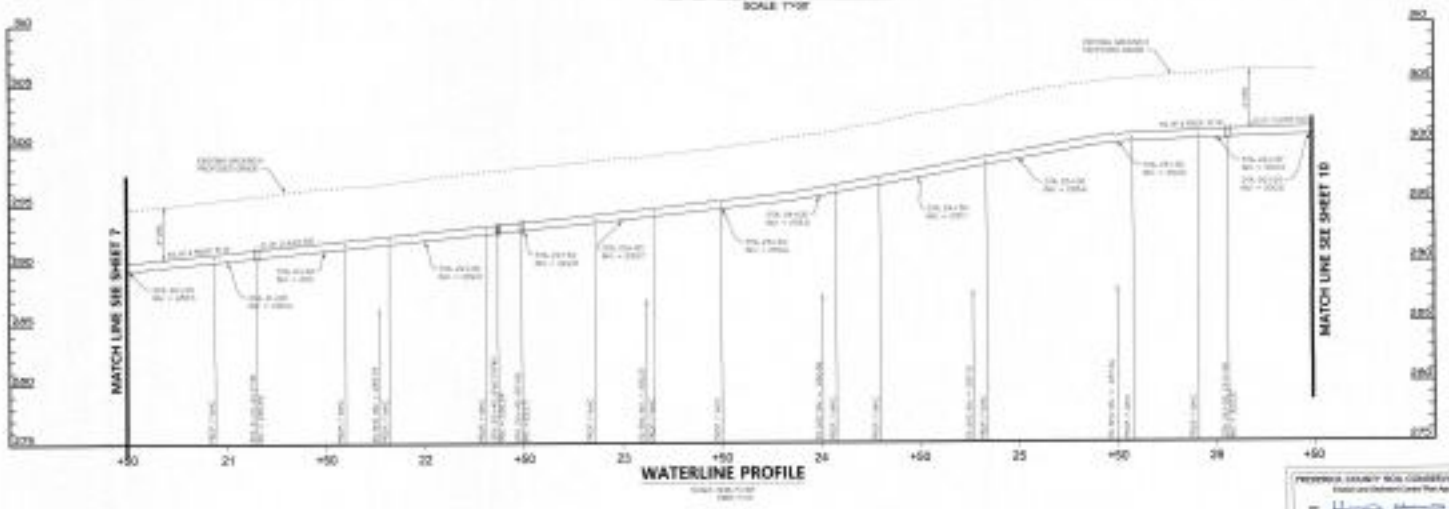

WATERLINE PROFILE

DMW

INSPIRATION AVENUE
PLAN & PROFILE

DISCOVERY PHASE - I
WATER MAIN
REPLACEMENT PROGRAM

OWNER / DEVELOPER

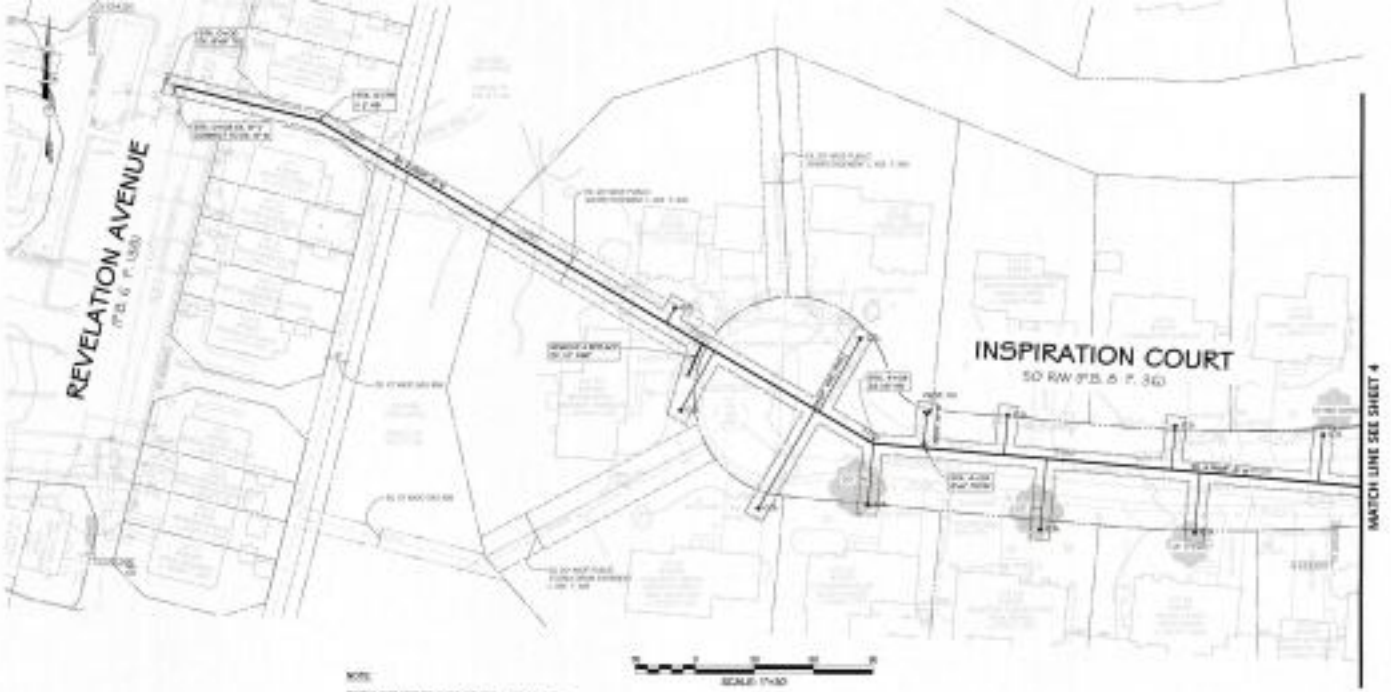

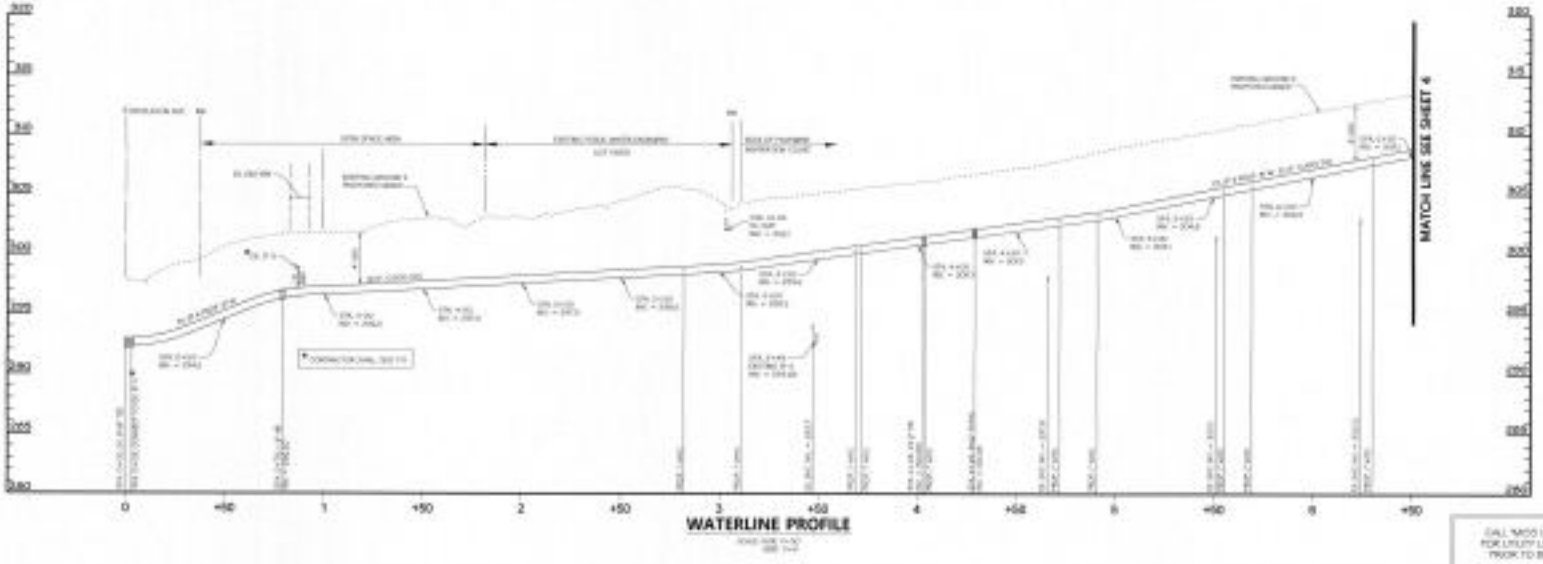

INSPIRATION COURT PLAN & PROFILE

DISCOVERY PHASE - I

WATER MAIN REPLACEMENT PROGRAM

CALL NCO1 UTILITY AT 1-800-XXX-YYYY FOR UTILITY LOCATIONS AT LEAST 3 DAYS PRIOR TO BEGINNING CONSTRUCTION.

TOWN OF WALKERSVILLE

WATER MAIN REPLACEMENT PROGRAM

IMPROVEMENT PLANS

DISCOVERY PHASE 1

TITLE	SHEET No.
COVER SHEET	1
WATER DETAILS	2
INSPIRATION COURT	3
INSPIRATION COVER/AVERAGE PLAN & PROFILE	4
DISCOVERY BLVD. PLAN & PROFILE	5
DAWN COURT PLAN & PROFILE	6
INSPIRATION AVENUE PLAN & PROFILE	7
CURIOSITY COURT PLAN & PROFILE	8
INSPIRATION AVENUE PLAN & PROFILE	9
INSPIRATION AVENUE PLAN & PROFILE	10
O'QUEFFE-KINSMAN CUTOFF 10" WMY PLAN & PROFILE	11
INSPIRATION AVENUE PLAN & PROFILE	12
"DISCIPLINARY" COURT PLAN & PROFILE	13
INSPIRATION AVE./IMAGINATION CT. PLAN & PROFILE	14
IMAGINATION COURT PLAN & PROFILE	15
SEDIMENT & EROSION CONTROL NOTES & DETAILS	16

LEGEND

EXISTING	DESCRIPTION	PROPOSED
	PROPERTY LINE	
	RIGHT-OF-WAY LINE	
	CENTER LINE	
	EASEMENT LINE	
	CONIFER TREE	
	DECIDUOUS TREE (OR AS SHOWN)	
	STORM MANHOLE & INLET	PROP. 77.10
	SANITARY MANHOLE & INLET	
	CATCH BASIN & INLET	
	SANITARY LATERAL	
	WATER MAIN & GATE VALVE	PROP. 8" W
	WATER METER	
	WATER VALVE	
	FIRE HYDRANT	
	GAS LINE	
	ELECTRIC LINE	
	UNDERGROUND TELEPHONE	
	OVERHEAD UTILITIES	
	UNDERGROUND UTILITIES	
	CURB & GUTTER	
	CONCRETE CURB	
	SITE ELEVATION	
	CONCRETE SLAB	
	STREET LIGHTING	
	PROJECT/FLOW DIRECTION	
	FIRE DEPARTMENT CONNECTION	
	BENCHMARK	
	ELEVATION OF ADJACENT BUILDING	
	BASE OF GARAGE SLAB	
	MAIL BOX	
	TELEPHONE/CABLE PEDESTAL	
	GAS VALVE	
	LIMIT OF DISTURBANCE	

SOIL AND KEY MAP

NOT TO SCALE

PROJECT SUMMARY

WATER LINE REPLACEMENT NOTES:

1. REPLACEMENT WATER SERVICE LINES OF 1" DIA. COPPER PIPE OR AS PER EXISTING WATER SERVICE LINES TO CONNECT TO EXISTING 8" WATER.
2. CONTRACTOR TO PROTECT AND ISOLATE EXISTING WATER VALVE TO BE USED AND WATER METER.
3. THE PROPOSED WATER DISTRIBUTION AS SHOWN OF WATER PLAN PLAN AND LAYOUT BY KOVATCH MARKS. CONTACT THE RESIDENT'S CLOSEST CONDITION OF WATER AND SEWER UTILITIES. EXISTING SUPERINTENDENT, WATER & MAINTENANCE MAINTENANCE OF CITY AND OVER AND/OR WATER CONSTRUCTION. WATER IS RESTORED AND MAINTAINED AT 20 PSI TEST PSI TO LEAST 48 HOURS PRIOR TO LINE TEST BEFORE ANY CONNECTION.

FOR UTILITY WORK ONLY OR FOR CBR-OTE UTILITY WORK

1. CONTACT OHIO ONE CALL BEFORE TEST.
2. PLACE ALL EXCAVATED MATERIAL ON THE HIGH SIDE OF THE TRENCH.
3. CONSTRUCTION WORK IN LINE TO BE COMPLETED IN ONE DAY SO THAT ROAD CROSSING, EXISTING AND PROPOSED LINE OUTLET OF THE LINE HAS NO CONSTRUCTION.
4. ANY DAMAGED EXISTING MEASURES FOUND DURING OF CONSTRUCTION WILL BE REPAIRED.
5. AT THE COMPLETION OF EACH WORK SHIFT, CONTRACTOR SHALL BACKFILL ALL TRENCHES AND PROVIDE TEMPORARY PAVEMENT AROUND THE PUBLIC ROADWAY SHALL BE THE RESPONSIBILITY.

DRAINAGE NOTES:

1. SINCE THE PROPOSED WORK OVERLAYS OTHER IMPROVEMENT PLANS & DEVELOPMENT WORK, THIS PROJECT IS EXEMPT FROM THE PREVIOUS STORMWATER MANAGEMENT ORDINANCE, BUT NEW IMPROVEMENTS AREA IS PROPOSED, THEREFORE THE RUNOFF CURVE NUMBER WILL NOT CHANGE & CONTROL NOT REQUIRED FOR THESE DEVELOPMENTS.
2. THE NEW PROPOSED WORK WILL NOT INCREASE OR REDUCE THE NUMBER AND SIZE.
3. ALL DISTURBED AREAS SHALL BE RESTORED TO A CONFORMED OR BETTER CONDITION THAN WHICH PREVIOUSLY EXISTED.
4. BUSINESSES AREAS SHALL NOT EXPERIENCE IMPACT OTHER DISTURBANCE WITH REGARD TO DRAINAGE.
5. THE TOP OF ALL BACKFILL WATER LOCATIONS SHALL AND/OR OTHER PERVIOUS AREAS IS NOT TO BE COMPACTED.

SOILS:

DmB - DUBFIELD-WAGASTOWN-URBAN LAND COMPLEX, NON-RESTRICTED, 0% - 8%, NOT HIGHLY ERODIBLE

FmC - WAGASTOWN LOAM, NON-RESTRICTED, 8% - 15%, HIGHLY ERODIBLE

MrB - WAGASTOWN LOAM, NON-RESTRICTED, 0% - 8%, NOT HIGHLY ERODIBLE

RkB - WAGASTOWN GRAVELLY LOAM, NON-RESTRICTED, 0% - 3%, NOT HIGHLY ERODIBLE

RkB - WALKERSVILLE GRAVELLY LOAM, NON-RESTRICTED, 0% - 8%, NOT HIGHLY ERODIBLE

APPROVALS SUMMARY TABLE

FORMAT	APPLICABILITY: YES	APPLICABILITY: NO	TRACKING NO.	APPROVAL DATE	EXPIRATION DATE
SOIL CONSERVATION DISTRICT	X		N/A		
MAY NOT APPLY, BUT MAY REQUIRE		X			
MAY NOT FOR STORMWATER, WITHDRAWS WITH CONSTRUCTION ACTIVITY		X			
CULVERTS (NOT PVMT)		X			
OTHER		X			

CERTIFICATION OF THE ENCLOSED DATA SUBMITTED

FILE #: TOWN OF WALKERSVILLE

A/P #: PW276805

Due Date:

OWNER/DEVELOPER'S CERTIFICATION

FREDERICK COUNTY SOIL CONSERVATION DISTRICT

Review and Standards Control Plan Approval

By: _____

District Manager or Designee

Date: 7/13/06

Plan is effective 2 years from date of approval

Not approved for wetlands and stream impacts or encroachments per the Maryland Wetlands and Waterways Act. You must contact the Maryland Department of the Environment for a permit prior to any construction activities in wetlands or streams or within their buffers.

PROFESSIONAL CERTIFICATION

I HEREBY CERTIFY THAT THESE DOCUMENTS WERE PREPARED OR APPROVED BY ME, AND THAT I AM A DULY LICENSED PROFESSIONAL ENGINEER UNDER THE LAWS OF THE STATE OF MARYLAND, LICENSE NO. 21222, EXPIRATION DATE: 07-09-2007

DMW

COVER SHEET

DISCOVERY PHASE - 1

WATER MAIN REPLACEMENT PROGRAM

TOWN OF WALKERSVILLE

FREDERICK COUNTY, MARYLAND

OWNER / DEVELOPER

DATE	BY	REVISIONS
07/06/2006	MRC	TOWN, COUNTY & PUC COMMENTS
07/07/2006	MRC	PUC RESUBMISSION

SCALE: AS SHOWN

DRAWN: MRC

DESIGN: MRC

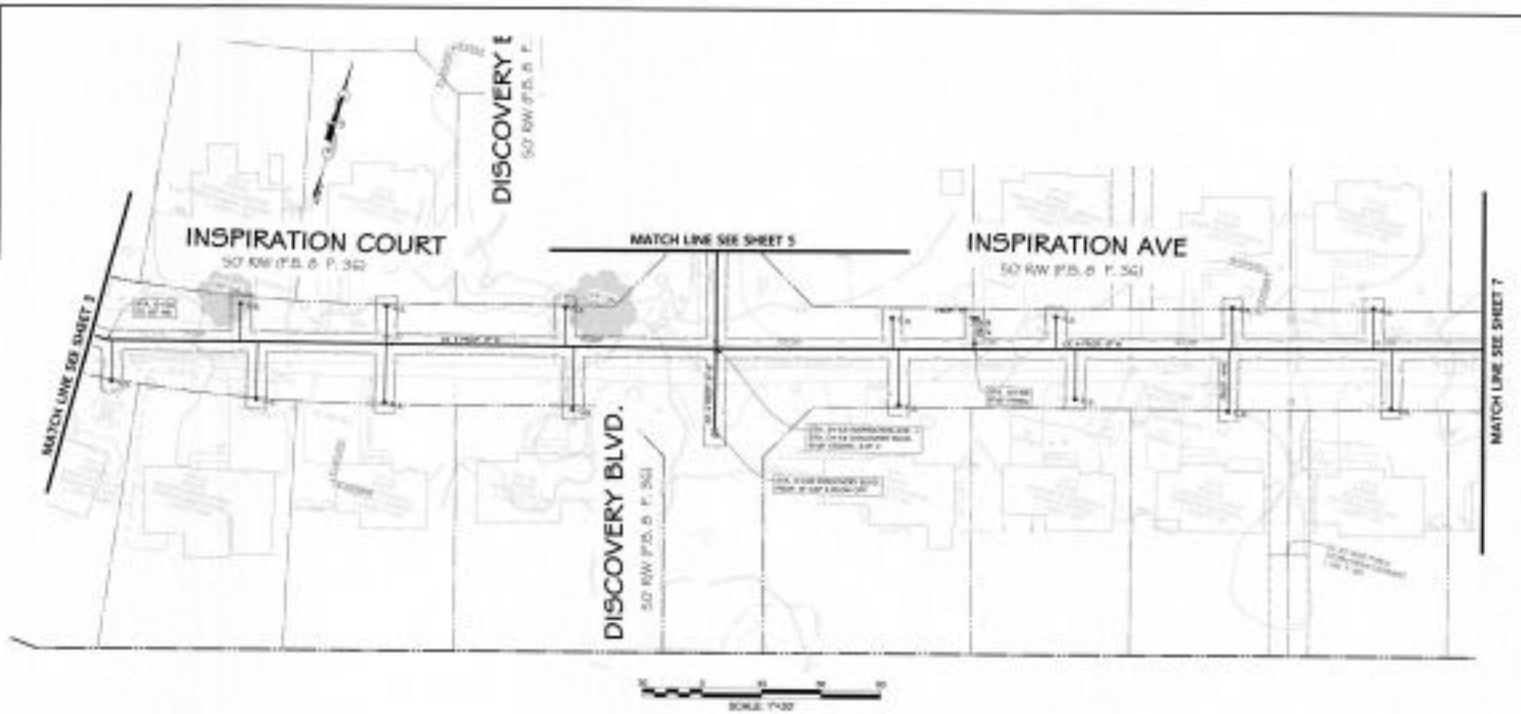

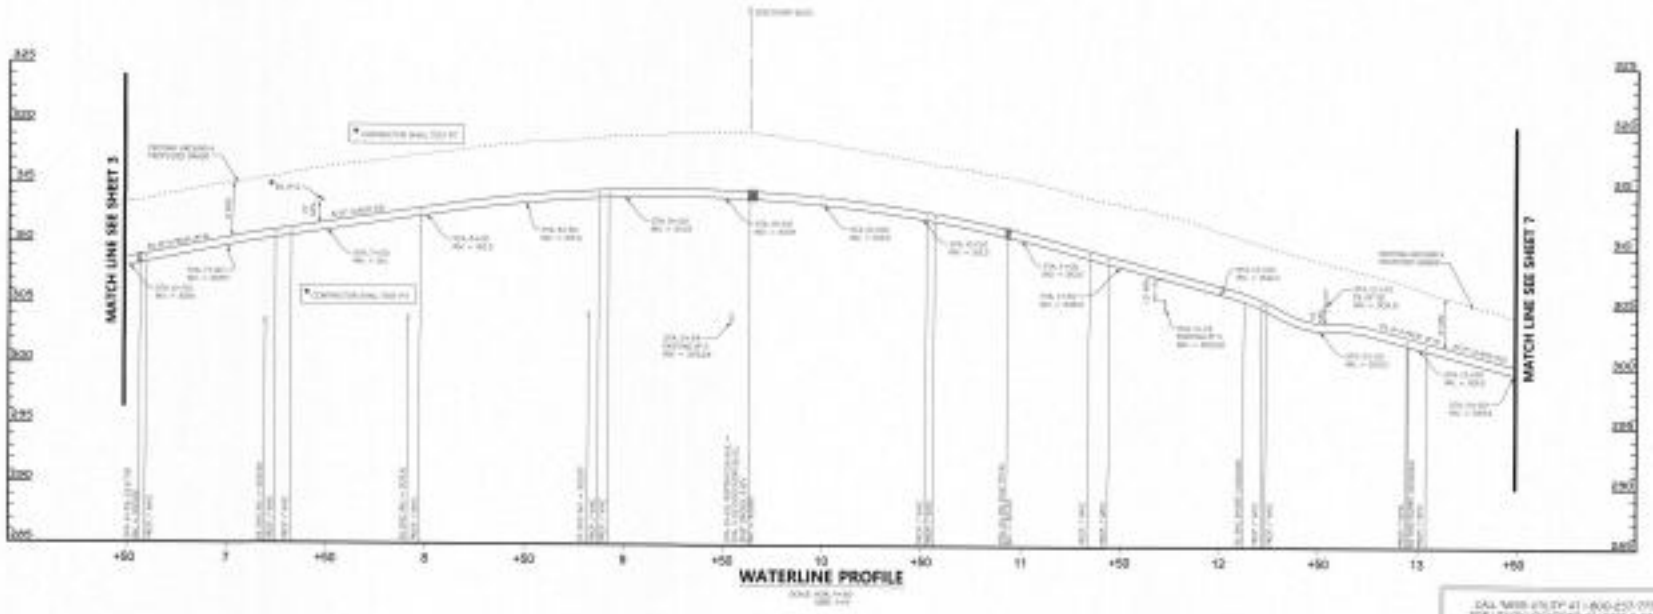

INSPIRATION CO
INSPIRATION AV
PLAN & PROF
DISCOVERY PH
WATER MAIN
REPLACEMENT PRO

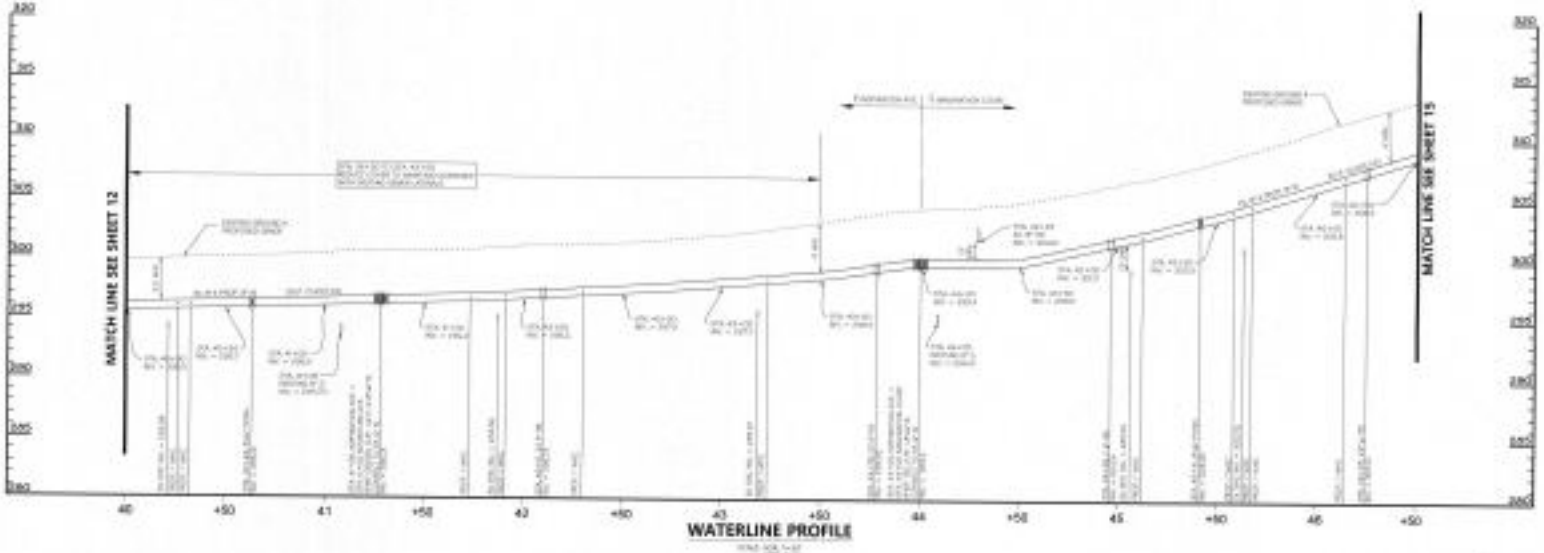

DMW

INSPIRATION AVENUE/
IMANGINATION COURT
PLAN & PROFILE
DISCOVERY PHASE - I
WATER MAIN
REPLACEMENT PROGRAM

OWNER / DEVELOPER

CALL MISS UTILITY AT 1-800-257-7777
FOR UTILITY LOCATIONS AT LEAST 5 DAYS
PRIOR TO BEGINNING CONSTRUCTION